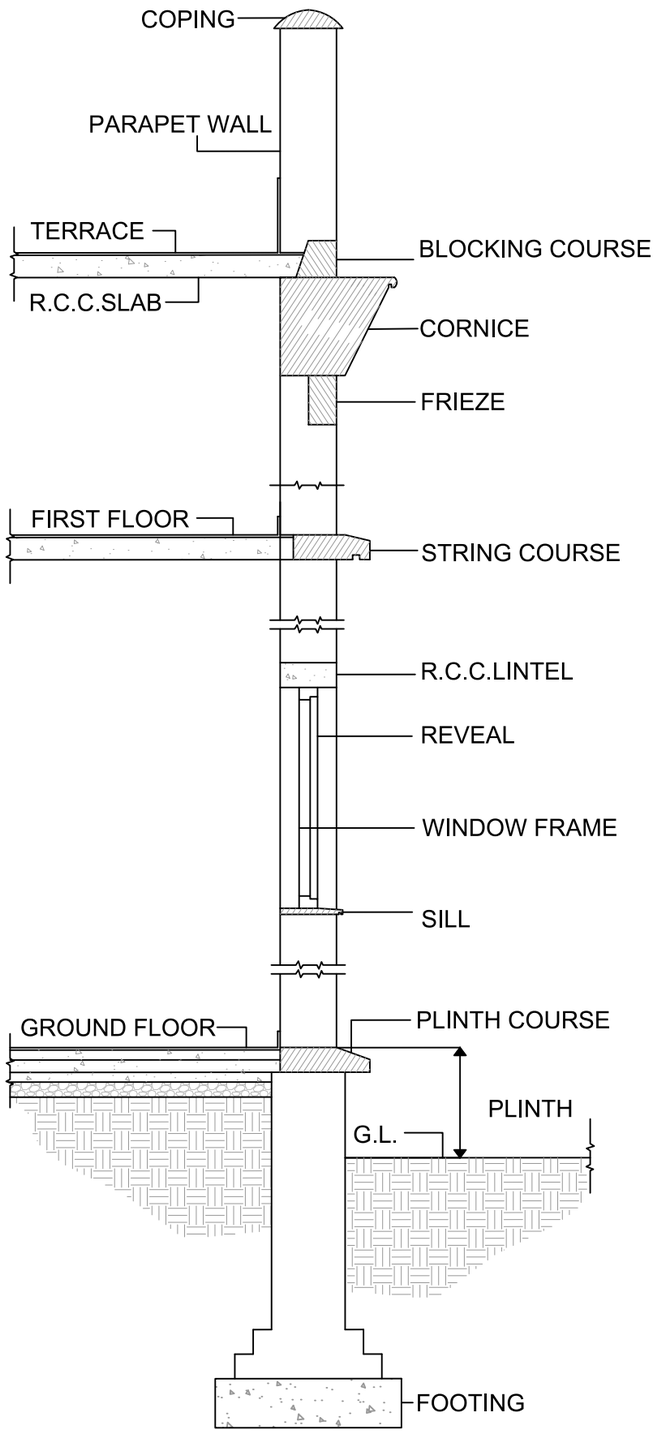

TITLE:

EXTERIOR WALL SECTION

SUBJECT: MATERIAL,CONSTRUCTION AND STRUCTURE
SHEET NO.: 02
SCALE: 1:25

NAME: HARSHITA PANWAR
ENROLLMENT NO.: 2403210006
PROGRAM.: BACHELORS OF DESIGN
YEAR: 2nd Year (4th Semester)

rishihood university

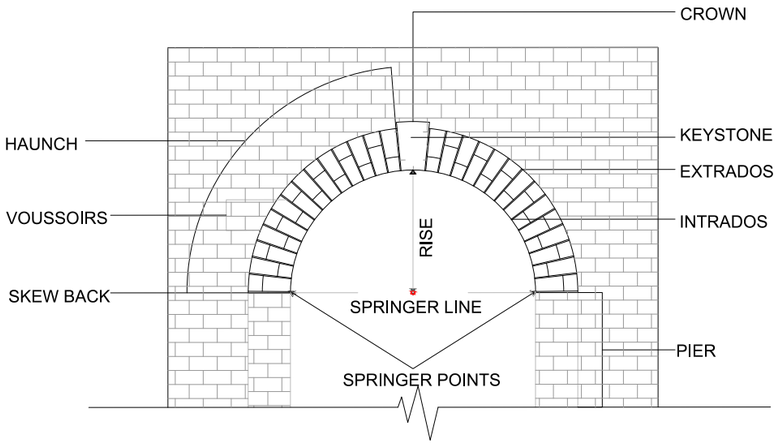

SEMI CIRCULAR ARCH

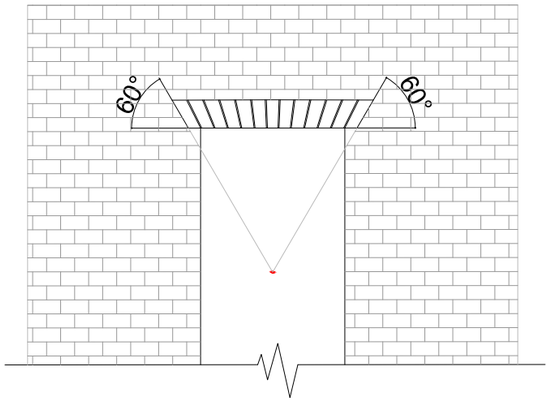

FLAT ARCH

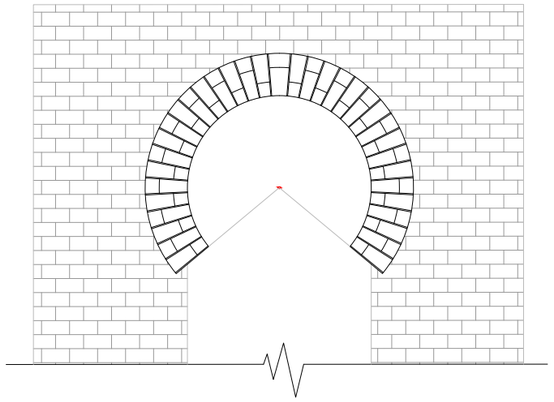

HORSE SHOE ARCH

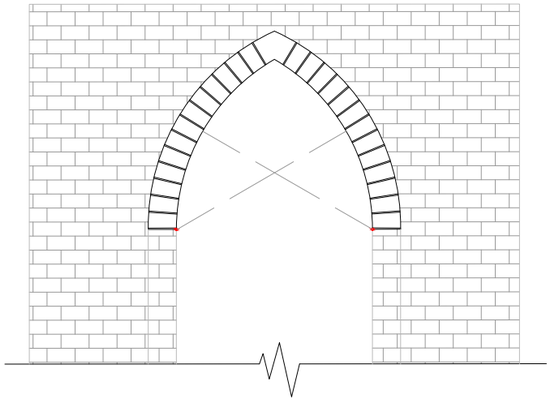

TWO-POINT ARCH

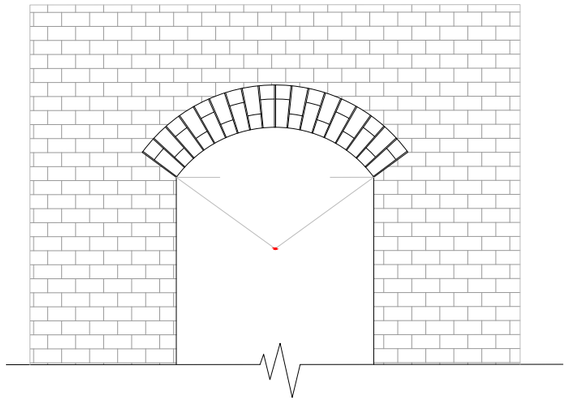

SEGMENTAL ARCH

TITLE:

ARCHES

SUBJECT: MATERIAL,CONSTRUCTION AND STRUCTURE
SHEET NO.: 03
SCALE: 1:50

NAME: HARSHITA PANWAR
ENROLLMENT NO.: 2403210006
PROGRAM.: BACHELORS OF DESIGN
YEAR: 2nd Year (4th Semester)

rishihood university

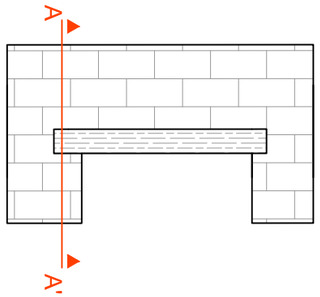

ELEVATION

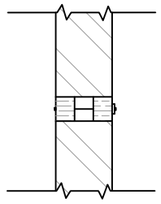

SECTION AA'

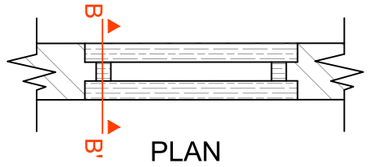

PLAN

SECTION BB'

TIMBER LINTEL

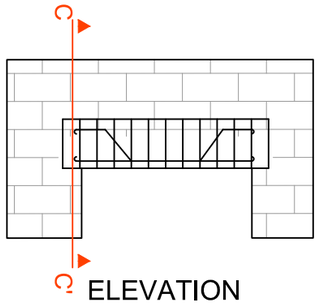

ELEVATION

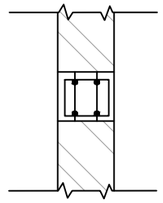

SECTION CC'

BRICK LINTEL

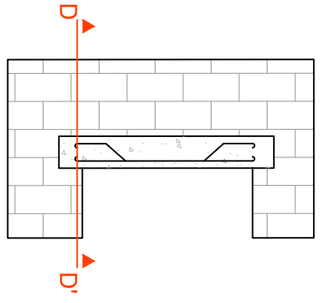

ELEVATION

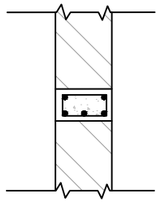

SECTION DD'

RCC LINTEL

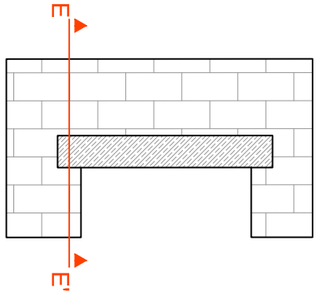

ELEVATION

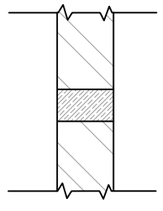

SECTION EE'

STONE LINTEL

TITLE:

LINTELS

SUBJECT: MATERIAL,CONSTRUCTION AND STRUCTURE
SHEET NO.: 04
SCALE: 1:25

NAME: HARSHITA PANWAR
ENROLLMENT NO.: 2403210006
PROGRAM.: BACHELORS OF DESIGN
YEAR: 2nd Year (4th Semester)

rishihood university

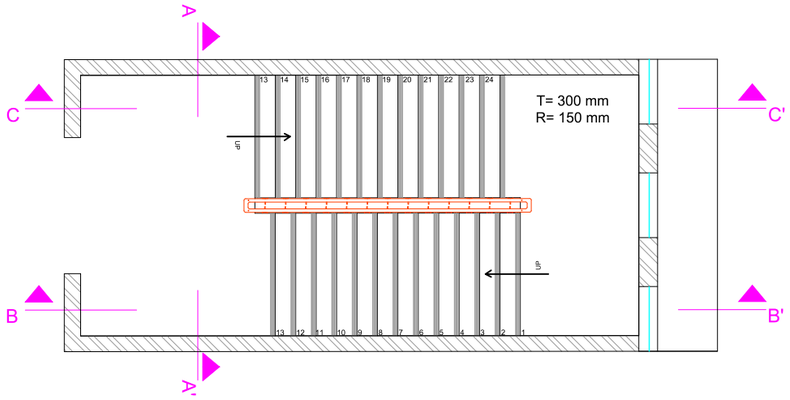

PLAN

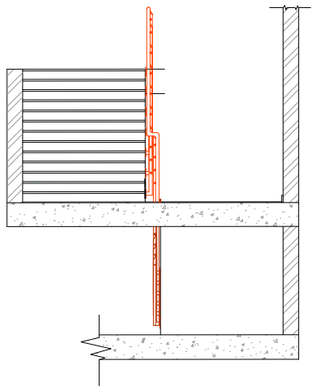

SECTION AA'

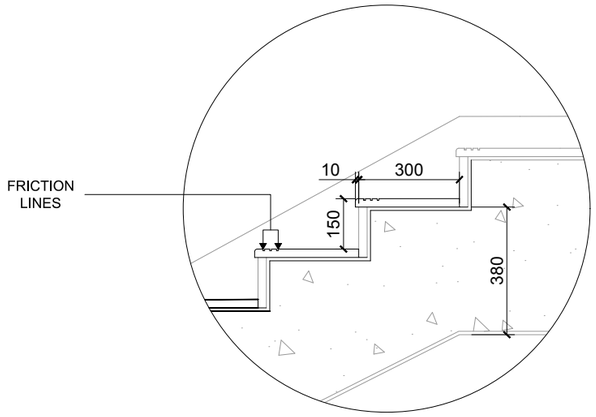

DETAILING

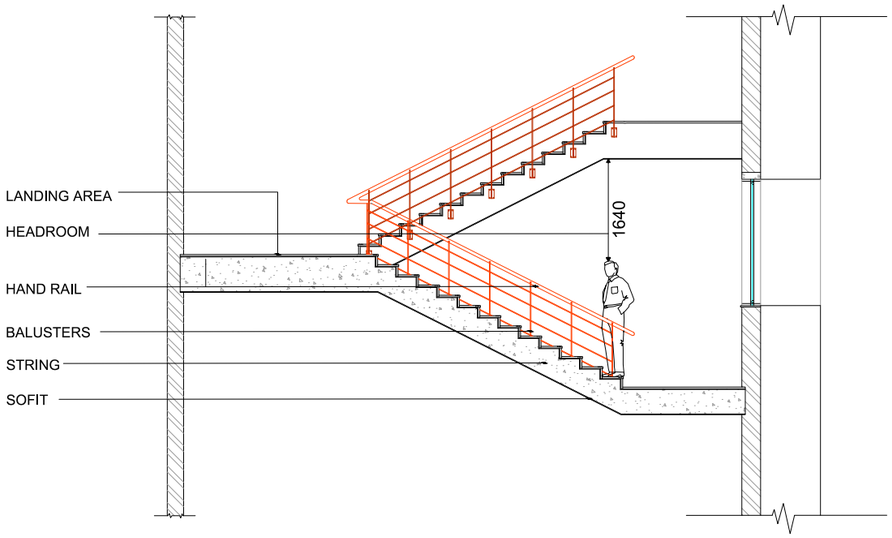

SECTION BB'

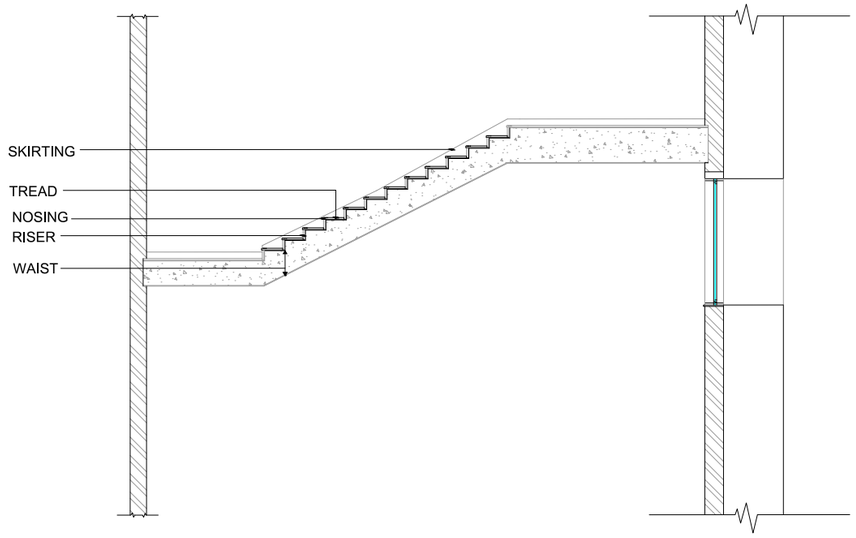

SECTION CC'

TITLE:

STAIRCASE

SUBJECT: MATERIAL,CONSTRUCTION AND STRUCTURE
SHEET NO.: 05
SCALE: 1:90

NAME: HARSHITA PANWAR
ENROLLMENT NO.: 2403210006
PROGRAM.: BACHELORS OF DESIGN
YEAR: 2nd Year (4th Semester)

rishihood university